NEO DHQ
Proposed Design

IDF's Distribution

Primary IDF
C6300 - SW Core 01
C6300 - SW Core 02
C6300 - SW Agg 01
C6300 - SW Agg 02

Finance Floor
C6300 - Access Switch 01
C6100 - Access Switch 02
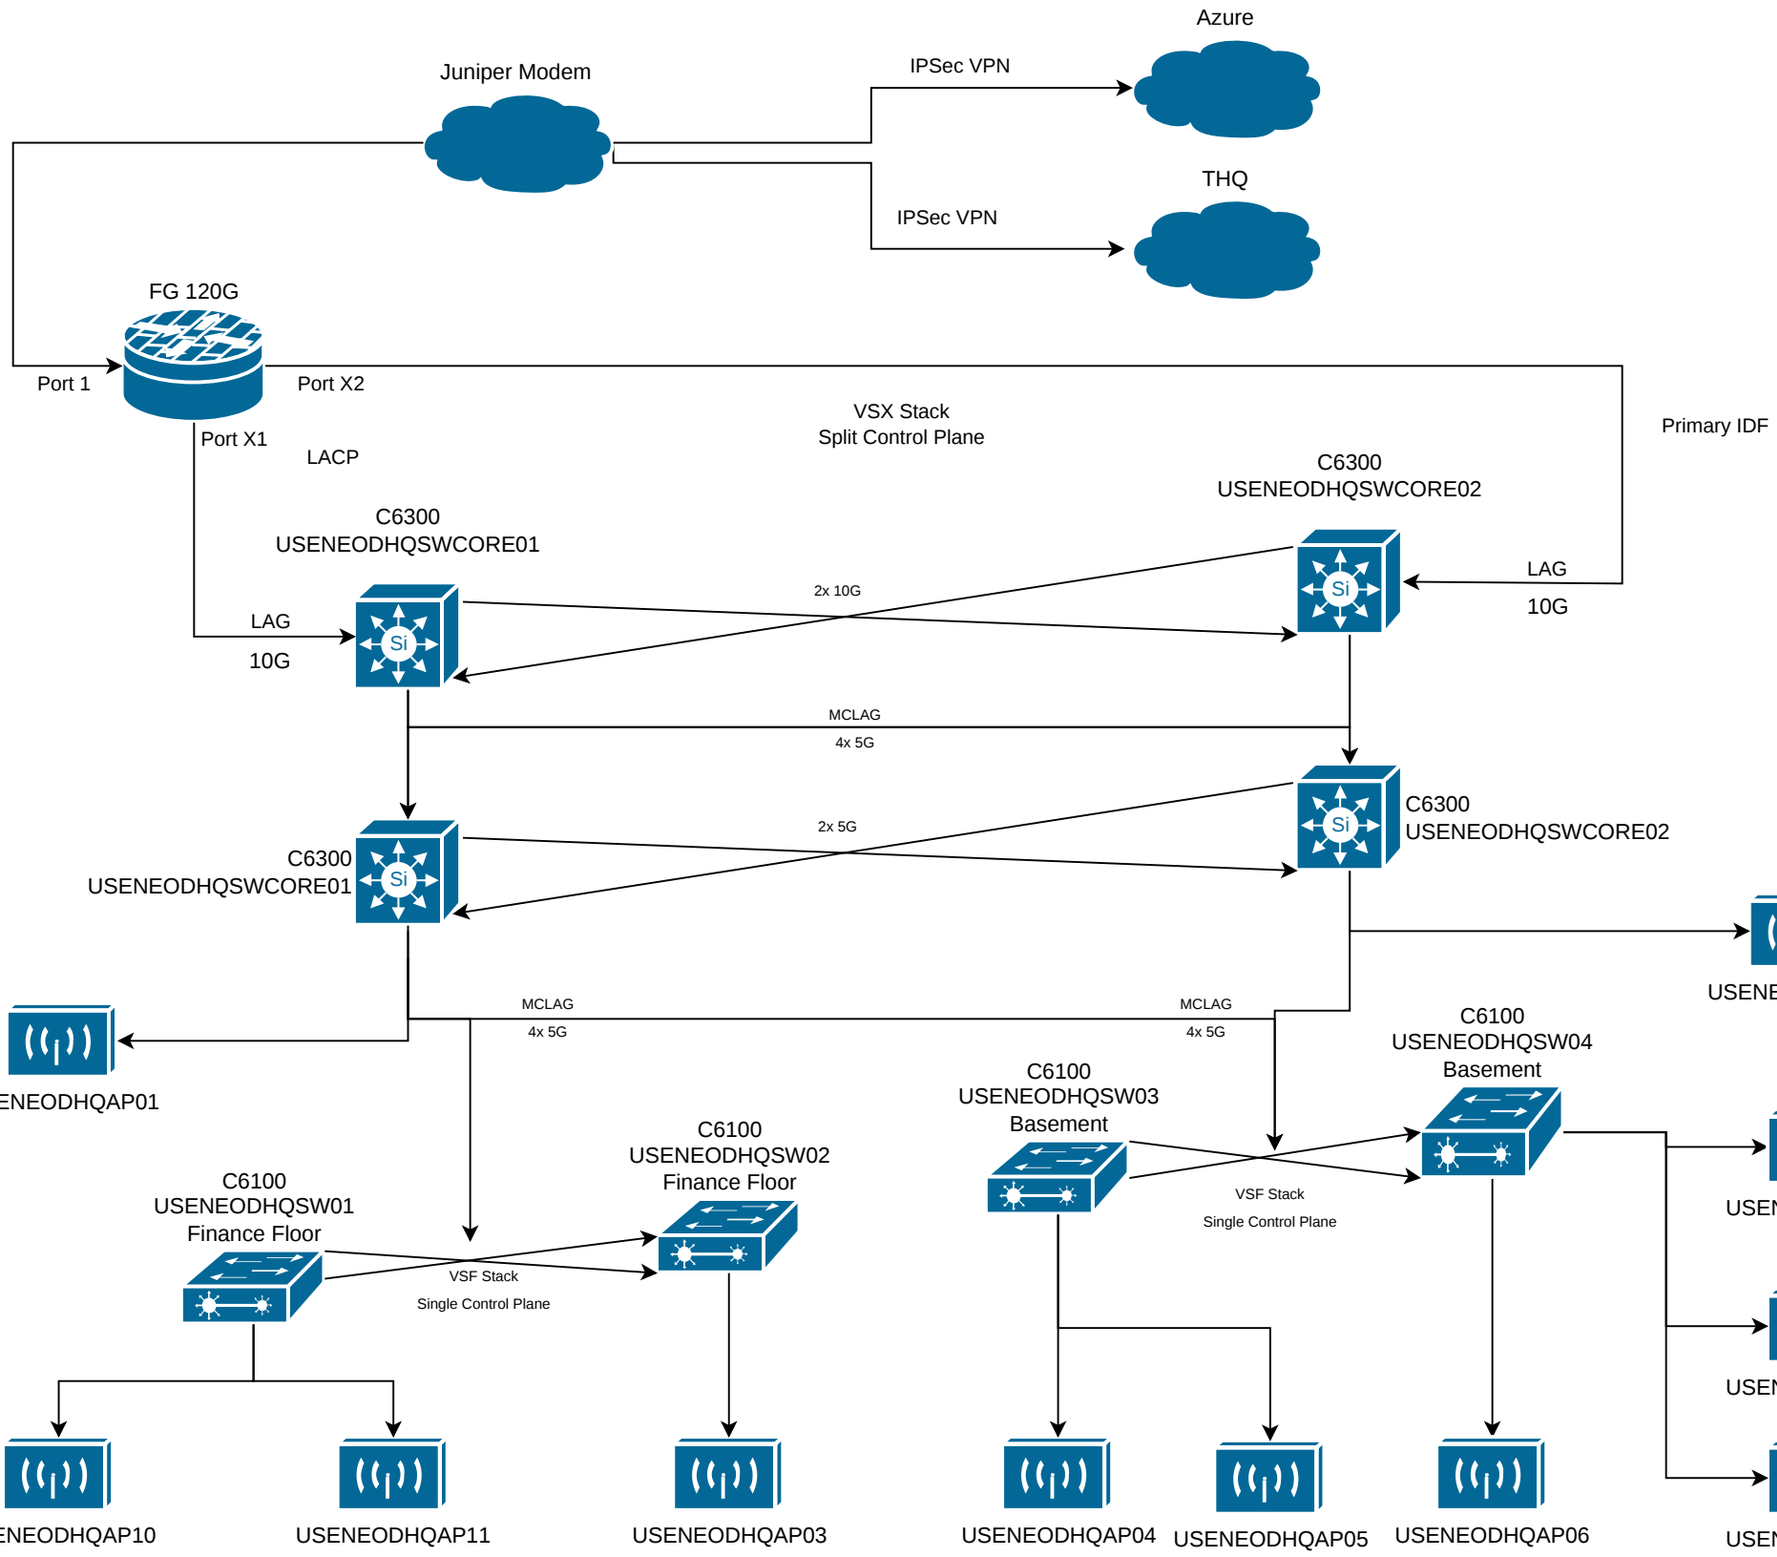
Recreation
C6100 - Access Switch 03
C6100 - Access Switch 04