


Kroc Dayton Ohio (SWO136)

Network Addressing
VLAN 1 - Default - 10.41.0.0/24
VLAN 100 - DMZ - 10.13.101.0/24
VLAN 101 - EFS - 10.25.140.0/24
VLAN 115 - SAUsers - 10.25.136.0/23
VLAN 150 - Guest - 10.25.142.0/24
VLAN 250 - HVAC - 10.25.139.0/26
VLAN 400 - Kroc Kiosks - 10.25.236.96/28
VLAN 450 - Dev_mgmt - 10.45.45.0/24
VLAN 460 - IoT_mgmt - 10.46.46.0/24
VLAN 500 - AV - 10.25.139.125/25
VLAN 750 - Security - 10.25.143.0/24

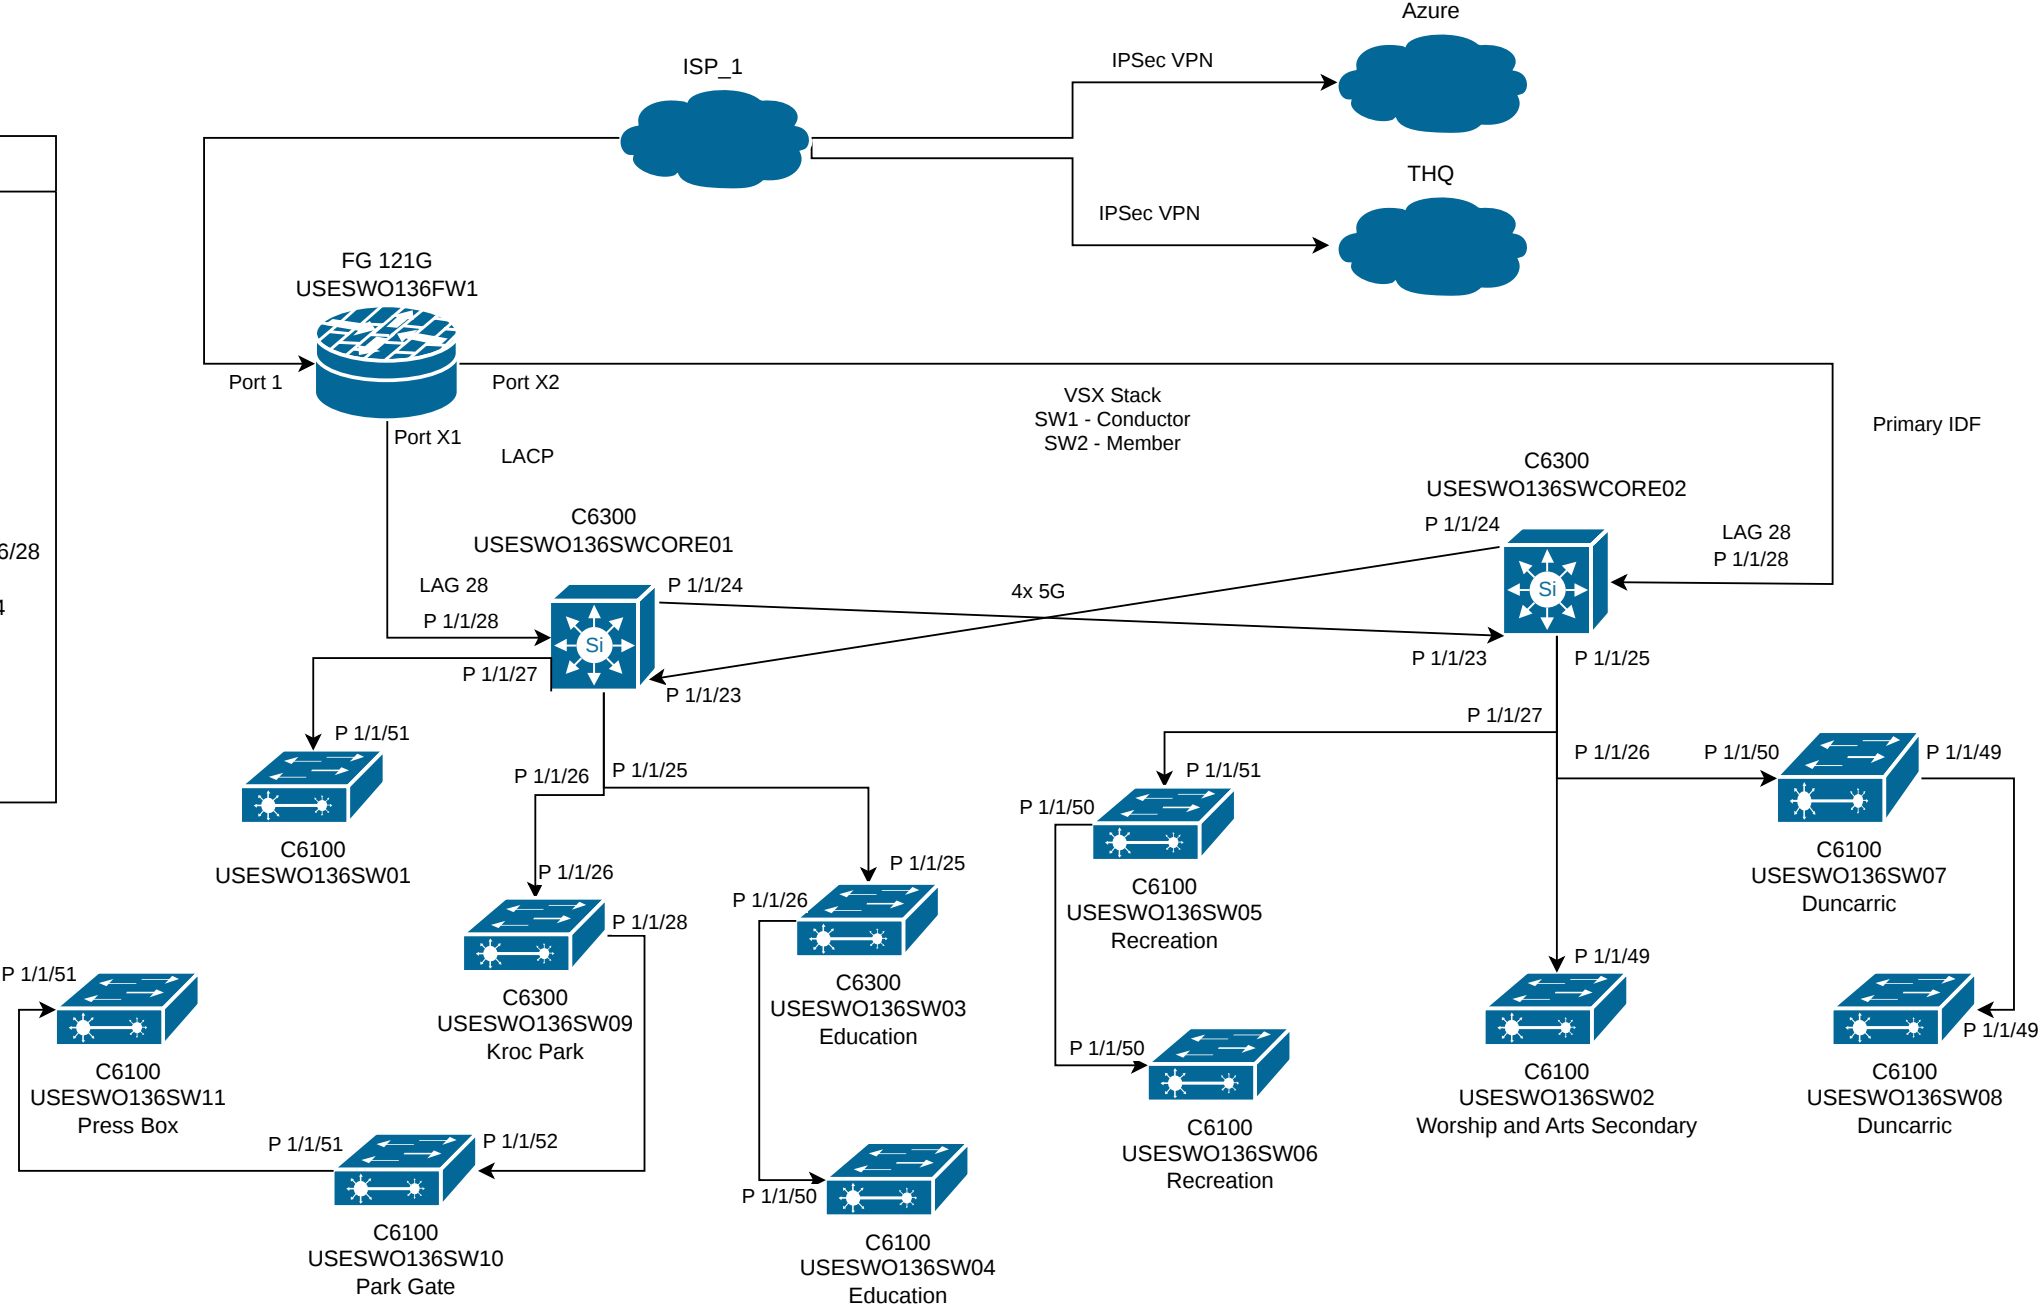

IDF's Distribution

Primary IDF	Worship and Arts	Education	Recreation	Duncarric	Kroc Park	Park Gate	Press Box
C6300 - SW Core 01	C6100 - Access Switch 02	C6300 - Access Switch 03	C6100 - Access Switch 05	C6100 - Access Switch 07	C6300 - Access Switch 09	C6100 - Access Switch 10	C6100 - Access Switch 11
C6300 - SW Core 02		C6100 - Access Switch 04	C6100 - Access Switch 06	C6100 - Access Switch 08			
C6100 - Access Switch 01							